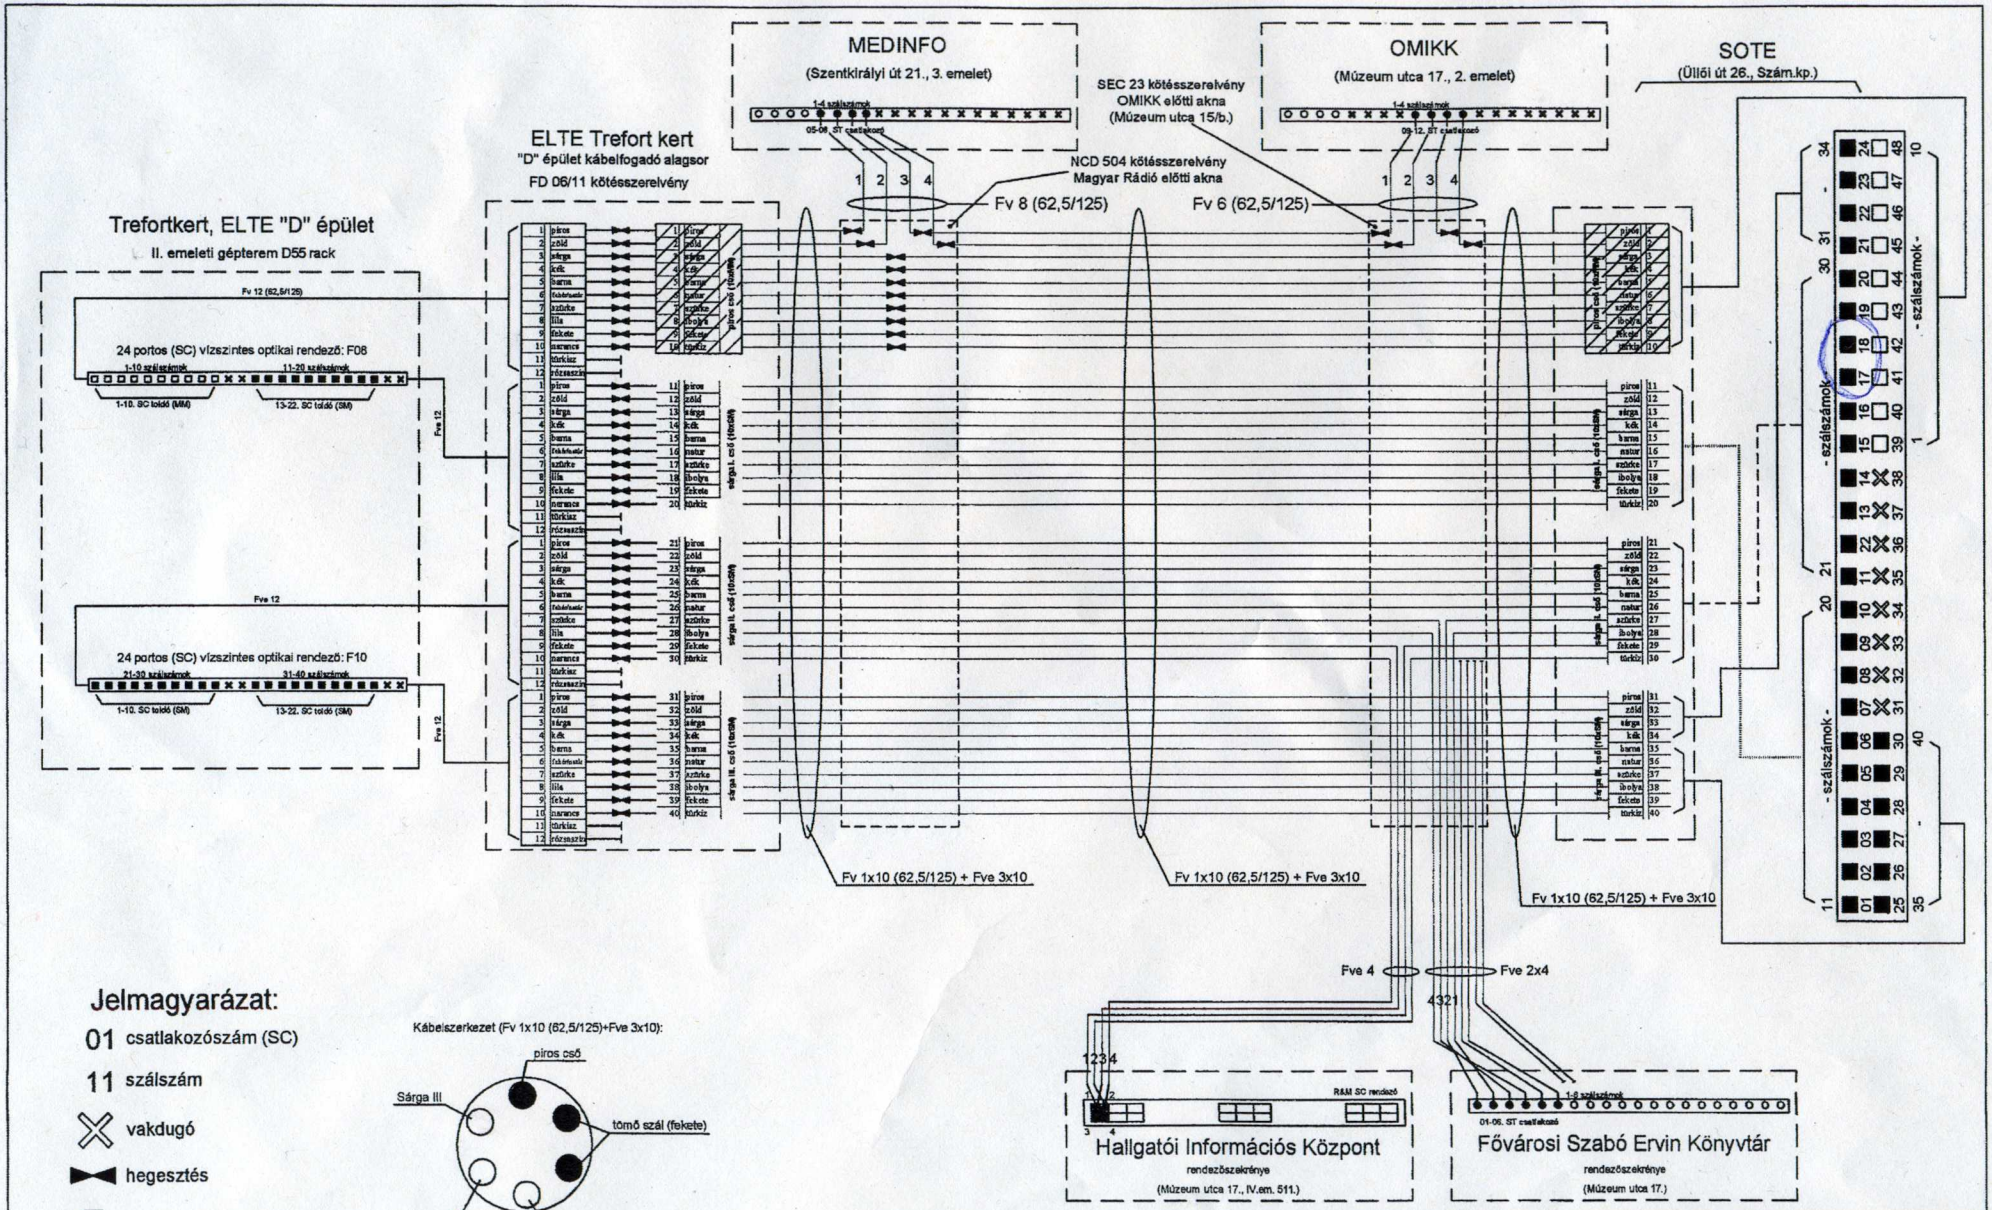
MEDINFO
(Szentkirályi út 21., 3. emelet)
OMIKK
(Múzeum utca 17., 2. emelet)
SOTE
(Üllői út 26., Szám.kp.)
SEC 23 kötésszerelvény
OMIKK előtti akna
(Múzeum utca 15/b.)
ELTE Trefort kert
"D" épület kábelfogadó alagsor
FD 06/11 kötésszerelvény
NCD 504 kötésszerelvény
Magyar Rádió előtti akna
Fv 8 (62,5/125)
Fv 6 (62,5/125)
Trefortkert, ELTE "D" épület
II. emeleti gépterem D55 rack
24 portos (SC) vízszintes optikai rendező: F08
24 portos (SC) vízszintes optikai rendező: F10
Fv 1x10 (62,5/125) + Fve 3x10
Fve 4
Fve 2x4
Hallgatói Információs Központ
rendezőszekrénye
(Múzeum utca 17., IV.em. 511.)
Fővárosi Szabó Ervin Könyvtár
rendezőszekrénye
(Múzeum utca 17.)
Jelmagyarázat:
01 csatlakozószám (SC)
11 szálszám
vakdugó
hegesztés
SM port
MM port
48 portos SC optikai rendező
20 portos ST optikai rendező
Kábelszerkezet (Fv 1x10 (62,5/125)+Fve 3x10):
piros cső
Sárga III
tömő szál (fekete)
Sárga II
Sárga I
SYNERGON
Synergon Informatika Rt 1047 Budapest, Baross u. 91-95.
Email.:info@synergon.hu Internet:www.synergon.hu
Tel.: 06-1-399-5500 Fax.: 06-1-399-5599
PROJECT MEGNEVEZÉSE
Elte-Medinfo-Omikk-(HIK-SzEKT)-Sote
Optikai összeköttetés szálkiosztása
Tervezte: Kovács Viktor
Rajzolta: Kádár László
Ellenőrizte: Sipos Imre
Dátum: 2003.02.10.
File: 6.dwg
Rajz szám: 6. sz.